


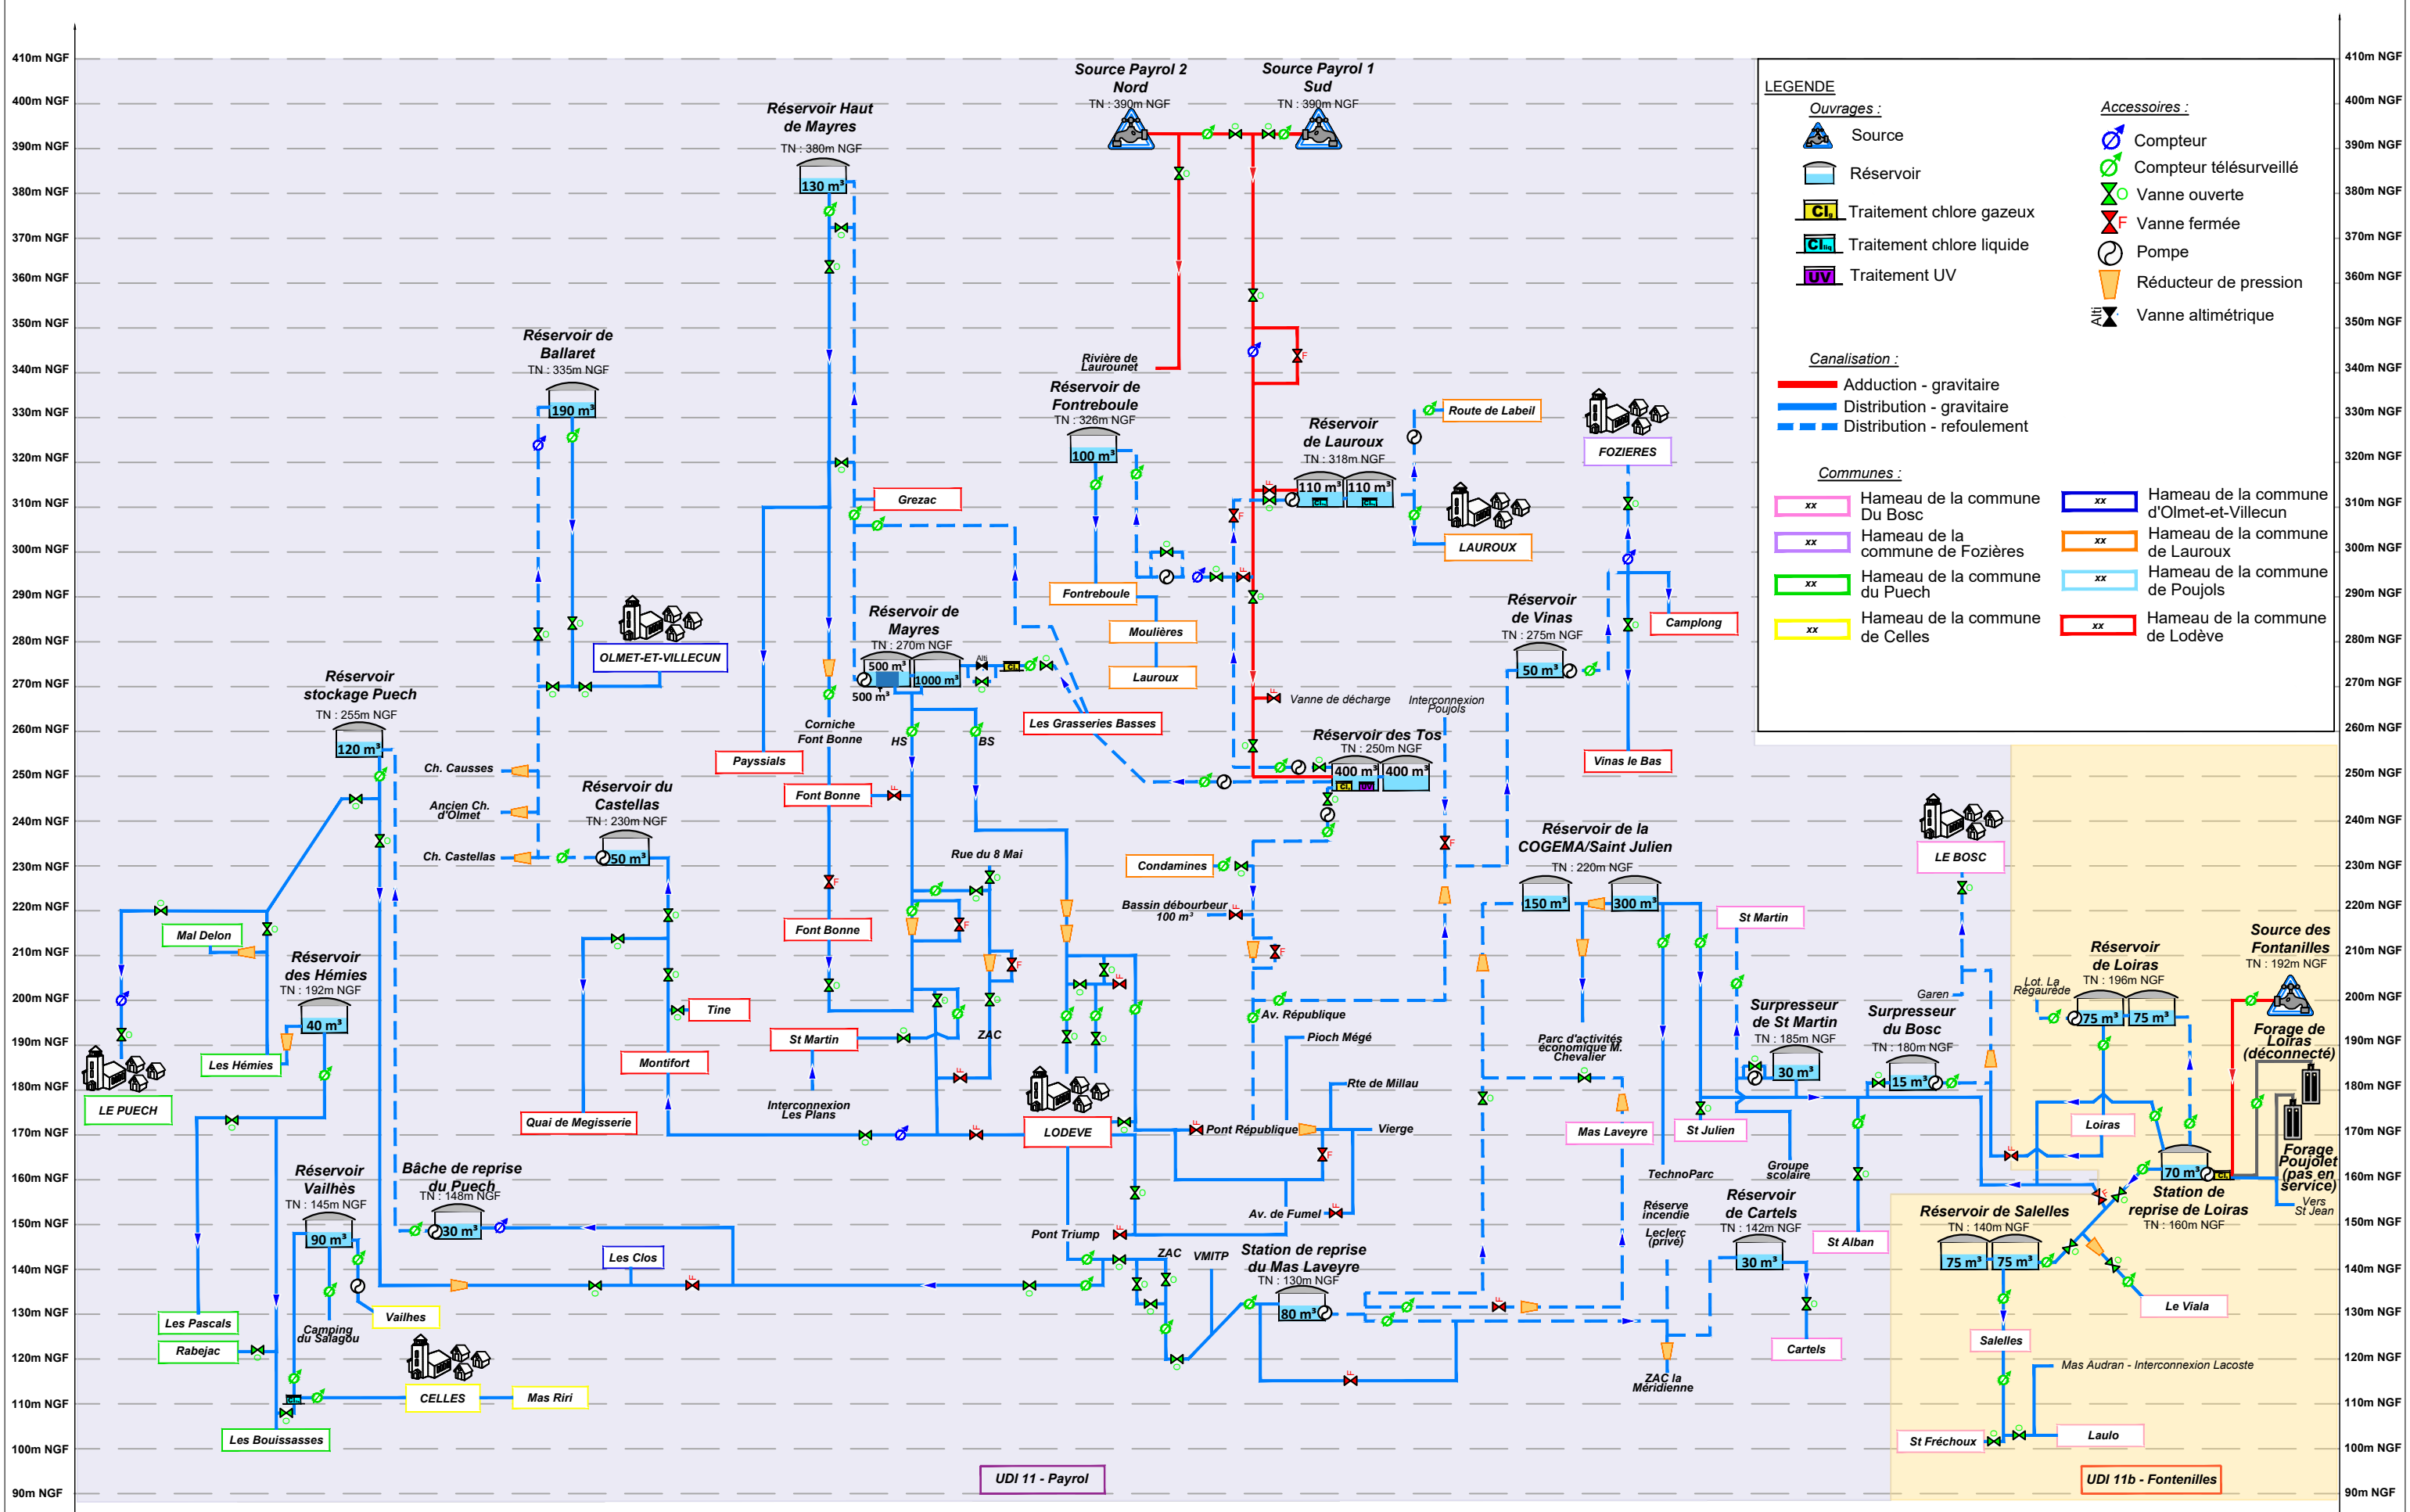

LEGENDE

Ouvrages :

- Source
- Réservoir
- CL_g Traitement chlore gazeux
- CL_{liq} Traitement chlore liquide
- UV Traitement UV

Accessoires :

- Compteur
- Compteur télésurveillé
- Vanne ouverte
- Vanne fermée
- Pompe
- Réducteur de pression
- Vanne altimétrique

Canalisation :

- Adduction - gravitaire
- Distribution - gravitaire
- Distribution - refoulement

Communes :

xx	Hameau de la commune Du Bosc	xx	Hameau de la commune d'Olmet-et-Villecun
xx	Hameau de la commune de Fozières	xx	Hameau de la commune de Lauroux
xx	Hameau de la commune de Puech	xx	Hameau de la commune de Poujols
xx	Hameau de la commune de Celles	xx	Hameau de la commune de Lodève