



UDI 3 - Beaume-Boucart

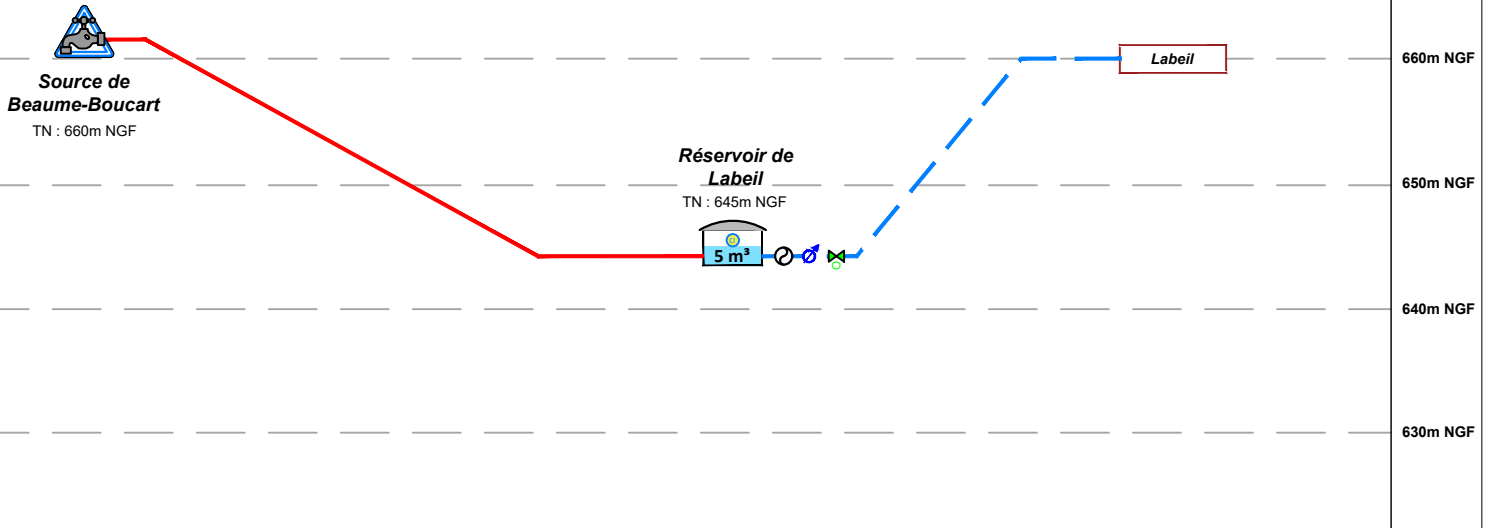


UDI 6 - Romiguières

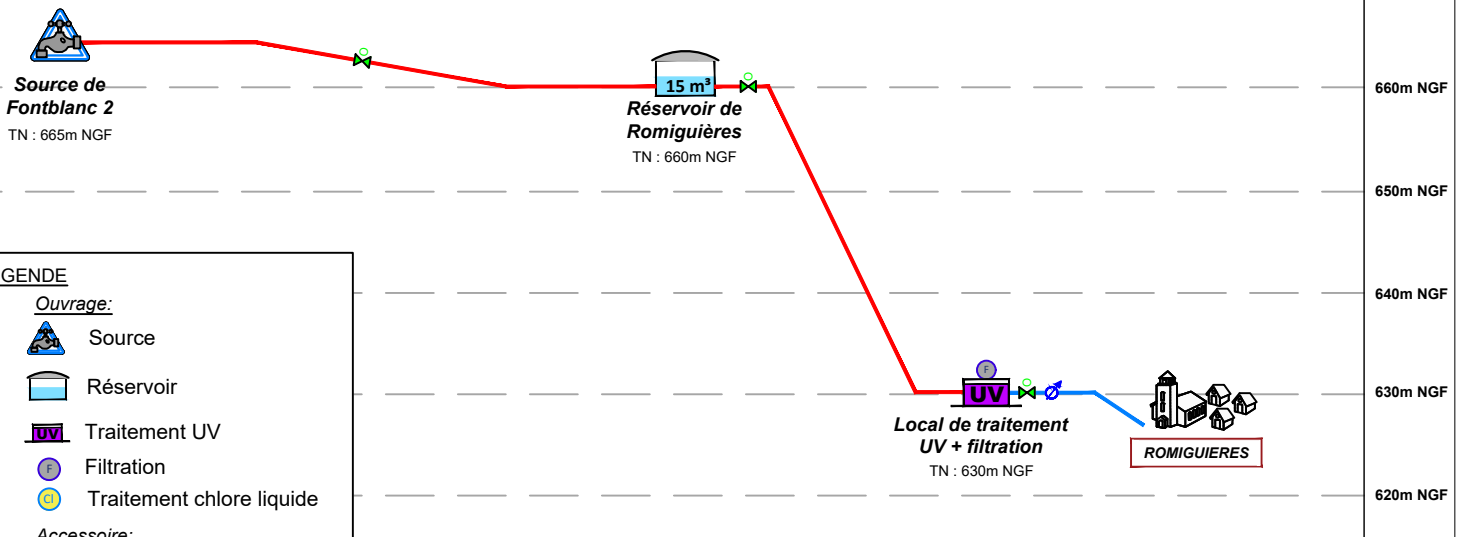

LEGENDE

Ouvrage:

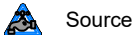

Source



Réservoir



Traitement UV



Filtration



Traitement chlore liquide

Accessoire:



Compteur non télésurveillé



Pompe



Vanne ouverte

Canalisation :



Adduction - gravitaire



Distribution - gravitaire



Distribution - refoulement

Communauté de Communes
Lodévois Larzac

SDAEP	A	Pas d'échelle
Décembre 2025		

Schéma Directeur d'Alimentation en Eau Potable
Synoptique de l'UDI 3 Beaume-Boucart et de l'UDI 6 Romiguières

Chef de projet : Florence ENJALBERT Ingénieur chargée d'affaire : Naïs DUSSART-MEZIERES Dessinatrice : Camille AUBERT N° affaire 24.053 Format A4