




UDI 7 - Soulages

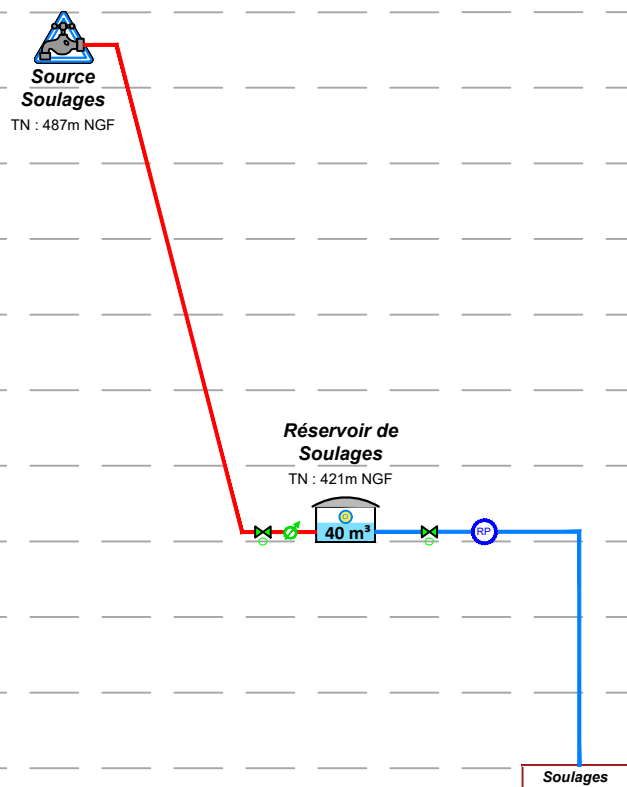

UDI 9 - Lambeyran

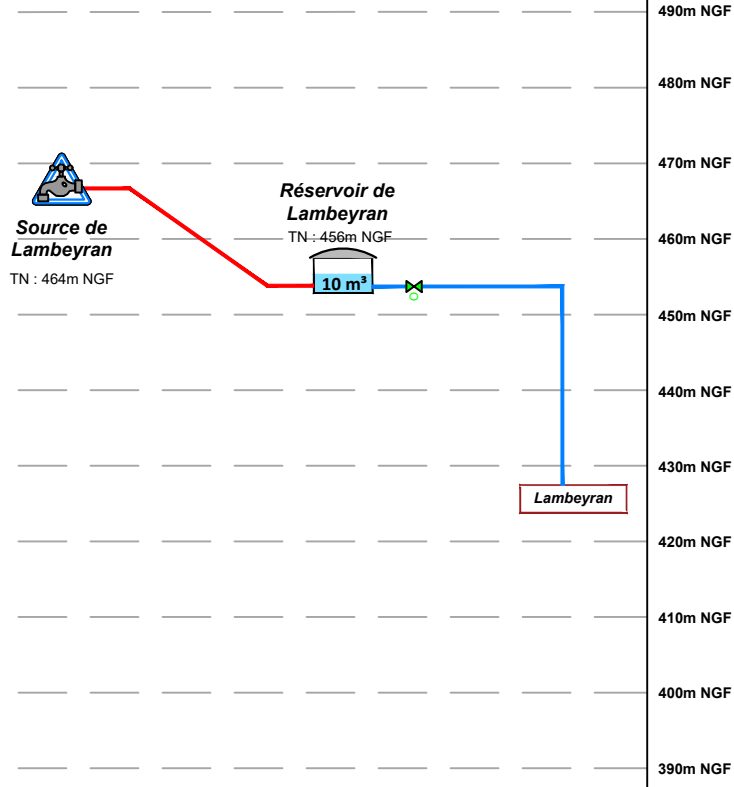

UDI 8 - Vernède

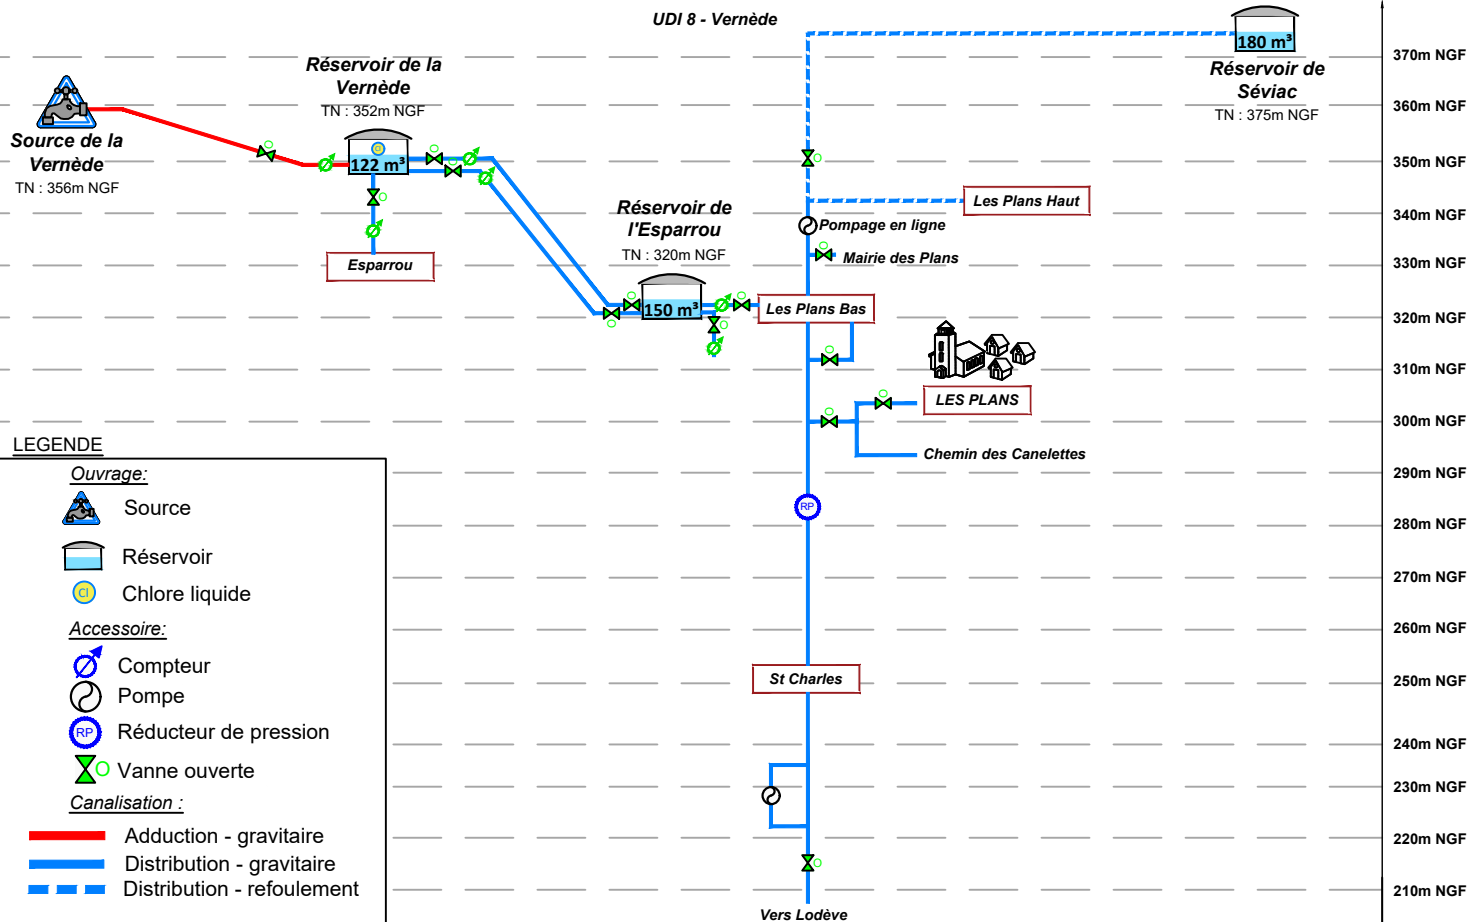

LEGENDE

Ouvrage:

- Source
- Réservoir
- Chlore liquide

Accessoire:

- Compteur
- Pompe
- Réducteur de pression
- Vanne ouverte

Canalisation:

- Adduction - gravitaire
- Distribution - gravitaire
- Distribution - refoulement



Communauté de Communes
Lodévois Larzac

SDAEP A Pas d'échelle
Décembre 2025

Schéma Directeur d'Alimentation en Eau Potable
Synoptique des UDI 7 Soulages, UDI 8 Vernède et 9 Lambeyran

Chef de projet : Florence ENJALBERT Ingénieur chargée d'affaire : Naïs DUSSART-MEZIERES Dessinatrice: Camille AUBERT (N° affaire) 24.053 Format A4